


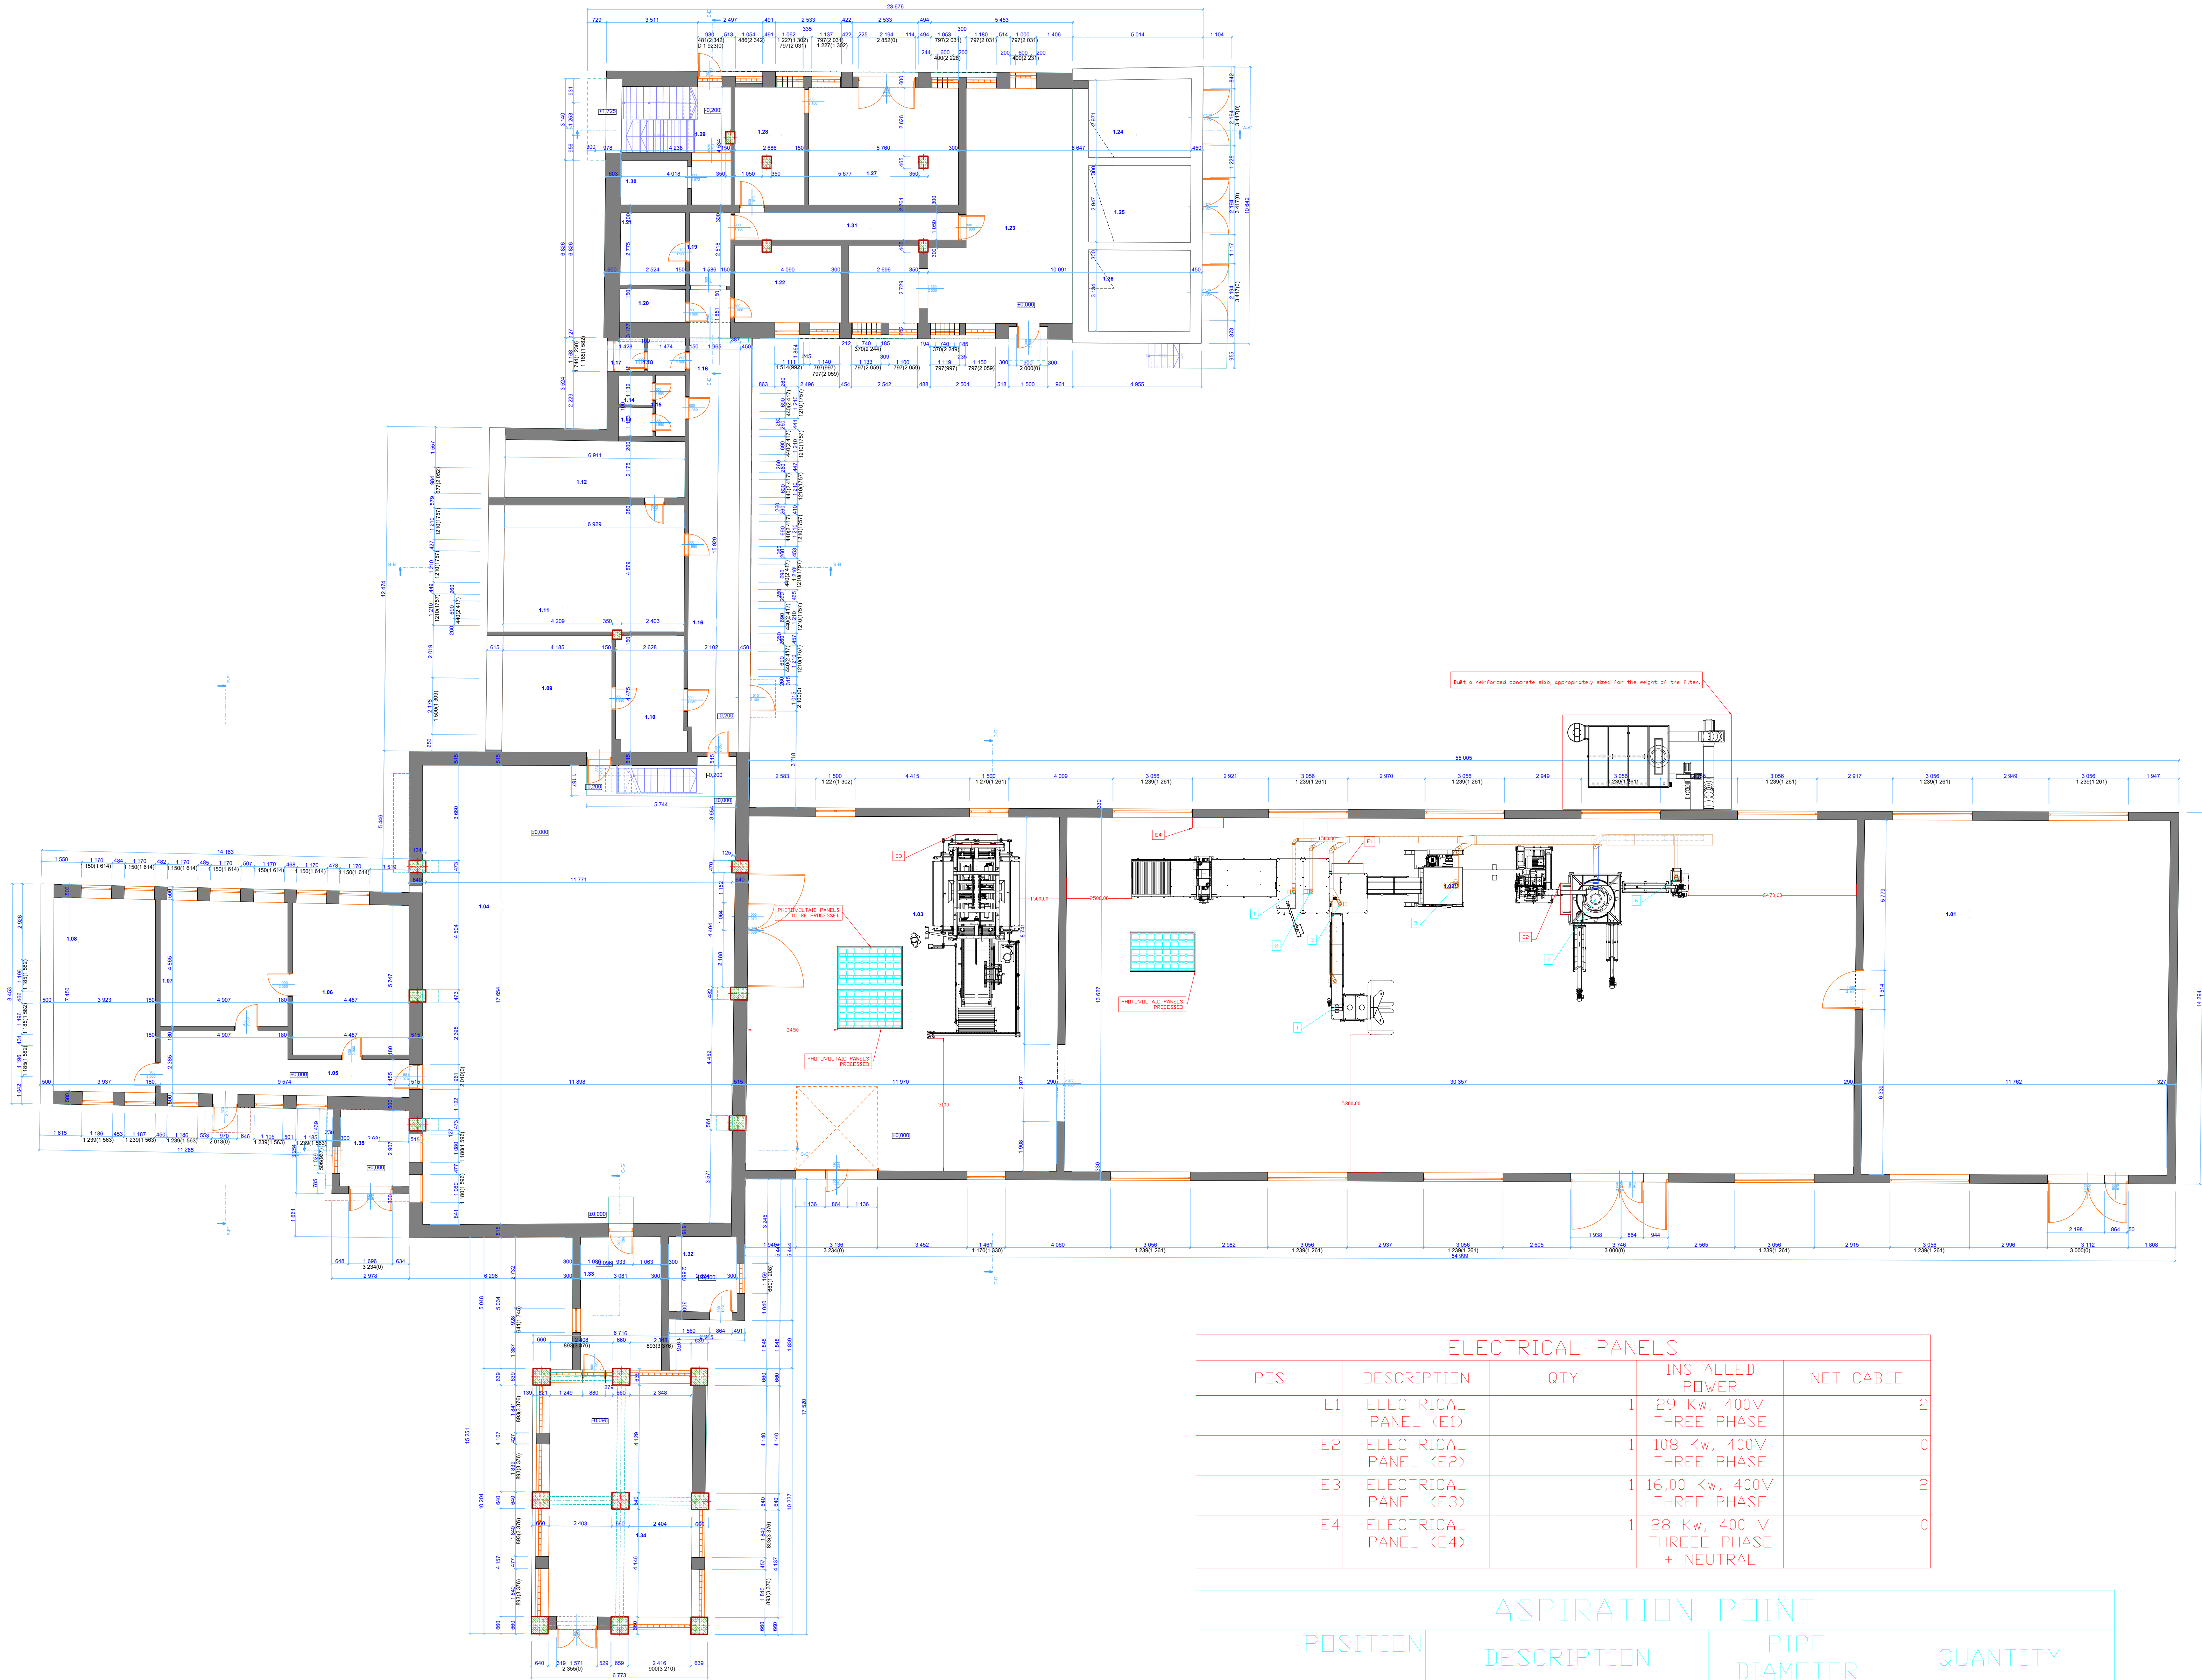

ELECTRICAL PANELS				
POS	DESCRIPTION	QTY	INSTALLED POWER	NET CABLE
E1	ELECTRICAL PANEL (E1)	1	29 Kw, 400V THREE PHASE	2
E2	ELECTRICAL PANEL (E2)	1	108 Kw, 400V THREE PHASE	0
E3	ELECTRICAL PANEL (E3)	1	16,00 Kw, 400V THREE PHASE	2
E4	ELECTRICAL PANEL (E4)	1	28 Kw, 400 V THREEE PHASE + NEUTRAL	0

ASPIRATION POINT			
POSITION	DESCRIPTION	PIPE DIAMETER	QUANTITY
1	DELAMINATOR	Ø120	1
2	DELAMINATOR	Ø120	1
3	CONNECTING CONVEYOR BELT	Ø120	1
4	DISCHARGE GLASS CONVEYOR BELT	Ø120	1
5	SHREDDER	Ø200	1
6	DENSIMETRIC TABLE	Ø120	1
7	PNEUMATIC TRANSPORT	Ø200	1